АДМИНИСТРАЦИЯ ГОРОДА ЕКАТЕРИНБУРГА

Градостроительный план земельного участка №

Р	Ф	-	6	6	-	3	-	0	2	-	0	-	0	0	-	2	0	2	4	-	2	1	8	5	-	0

Местонахождение земельного участка: Российская Федерация, Свердловская область, г. Екатеринбург

г. Екатеринбург

АДМИНИСТРАЦИЯ ГОРОДА ЕКАТЕРИНБУРГА

Градостроительный план земельного участка №

РФ-66-3-02-0-00-2024-2185-0

Градостроительный план земельного участка подготовлен на основании заявления:
ООО "Специализированный Застройщик "Свобода Мысли" №12299/003/21/001 от 30.07.2024

(реквизиты заявления правообладателя земельного участка, иного лица в случае, предусмотренном частью 1.1 статьи 57.3 Градостроительного кодекса Российской Федерации, с указанием ф.и.о. заявителя – физического лица, либо реквизиты заявления и наименование заявителя – юридического лица о выдаче градостроительного плана земельного участка)

Местонахождение земельного участка:
Свердловская область

(субъект Российской Федерации)

Муниципальное образование «город Екатеринбург»

(муниципальный район или городской округ)

Свердловская область, г Екатеринбург, ул Депутатская

(поселение)

Описание границ земельного участка (образуемого земельного участка): см. Приложение №1

Кадастровый номер земельного участка (при наличии) или в случае, предусмотренном частью 1.1 и 1.2 статьи 57.3 Градостроительного кодекса Российской Федерации, условный номер образуемого земельного участка на основании утвержденных проекта межевания территории и (или) схемы расположения земельного участка или земельных участков на кадастровом плане территории:
66:41:0403044:148

Площадь земельного участка
5498 м²

Информация о расположенных в границах земельного участка объектах капитального строительства:
В границах земельного участка расположены объекты капитального строительства. Количество объектов капитального строительства 6 единиц(ы). Количество объектов культурного наследия 0 единиц(ы). Объекты отображаются на чертеже(ах) градостроительного плана под порядковыми номерами. Описание объектов капитального строительства приводится в подразделе 3.1 «Объекты капитального строительства» или подразделе 3.2 «Объекты, включенные в единый государственный реестр объектов культурного наследия (памятников истории и культуры) народов Российской Федерации» раздела 3

Информация о границах зоны планируемого размещения объекта капитального строительства в соответствии с утвержденным проектом планировки территории (при наличии)**:** см. Приложение №1

Реквизиты проекта планировки территории и (или) проекта межевания территории в случае, если земельный участок расположен в границах территории, в отношении которой утверждены проект планировки территории и (или) проект межевания территории:
Документация по планировке территории не утверждена

(указывается в случае, если земельный участок расположен в границах территории, в отношении которой утверждены проект планировки территории и (или) проект межевания территории)

Информация о расположении земельного участка в границах территории, в отношении которой принято решение о комплексном развитии территории и (или) заключен договор о комплексном развитии территории
-


(указывается в случае, если земельный участок расположен в границах территории, в отношении которой принято решение о комплексном развитии территории и (или) заключен договор о комплексном развитии территории)

Градостроительный план подготовлен Габдрахмановым Русланом Гайнельзяновичем, Директором Департамента архитектуры, градостроительства и регулирования земельных отношений Администрации города Екатеринбурга - главным архитектором

(ф.и.о., должность уполномоченного лица, наименование органа)

М.П. (при наличии) _____ (подпись) Р.Г.Габдрахманов (расшифровка подписи)

Дата выдачи 13.08.2024
(ДД.ММ.ГГГГ)

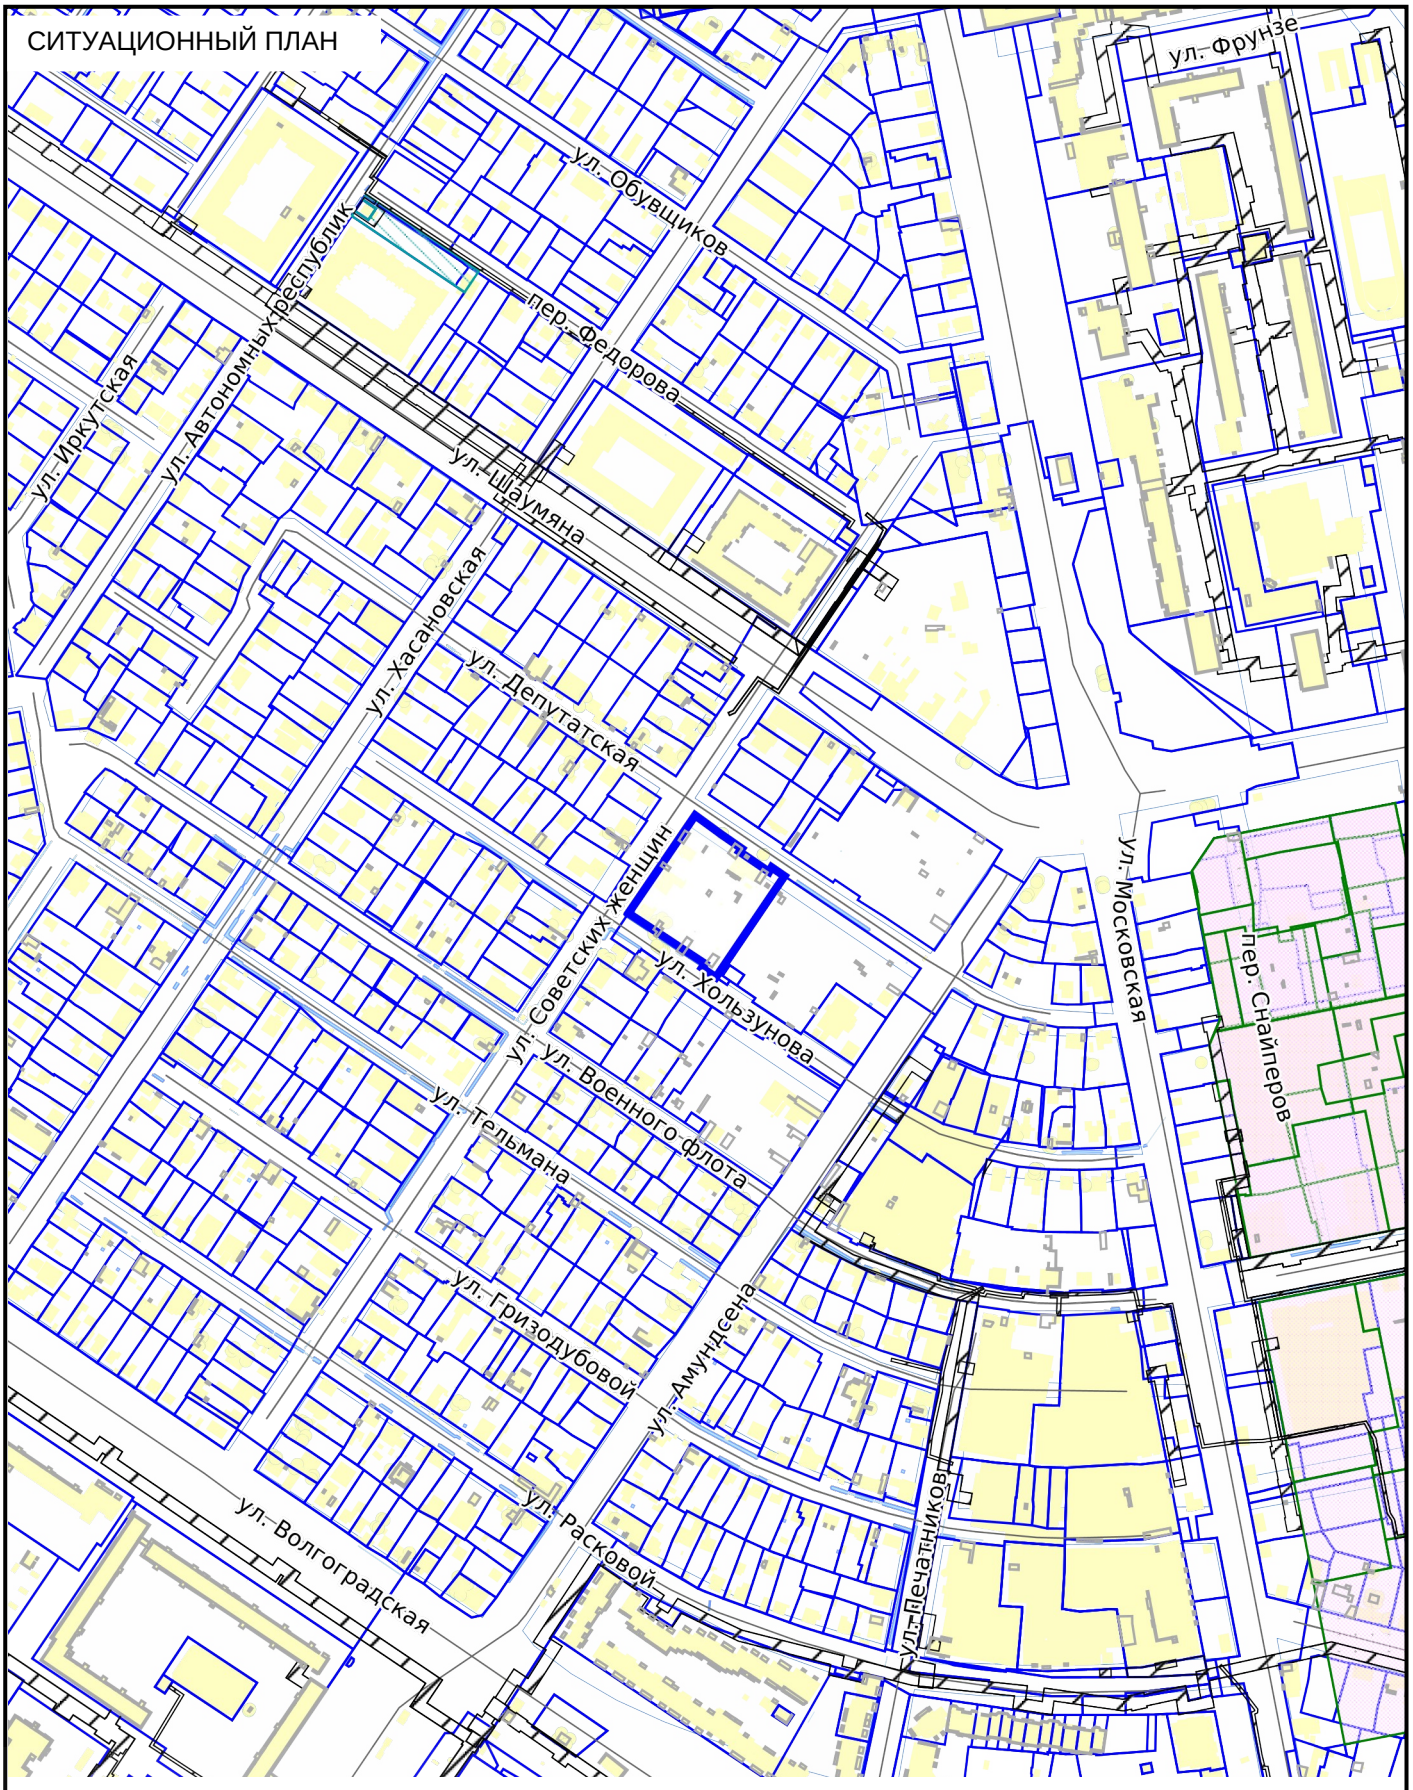


СИТУАЦИОННЫЙ ПЛАН

№ РФ-66-3-02-0-00-2024-2185-0

- Местоположение земельного участка

Масштаб	1:5000	Свердловская область, г Екатеринбург, ул Депутатская
Дата	13.08.2024	

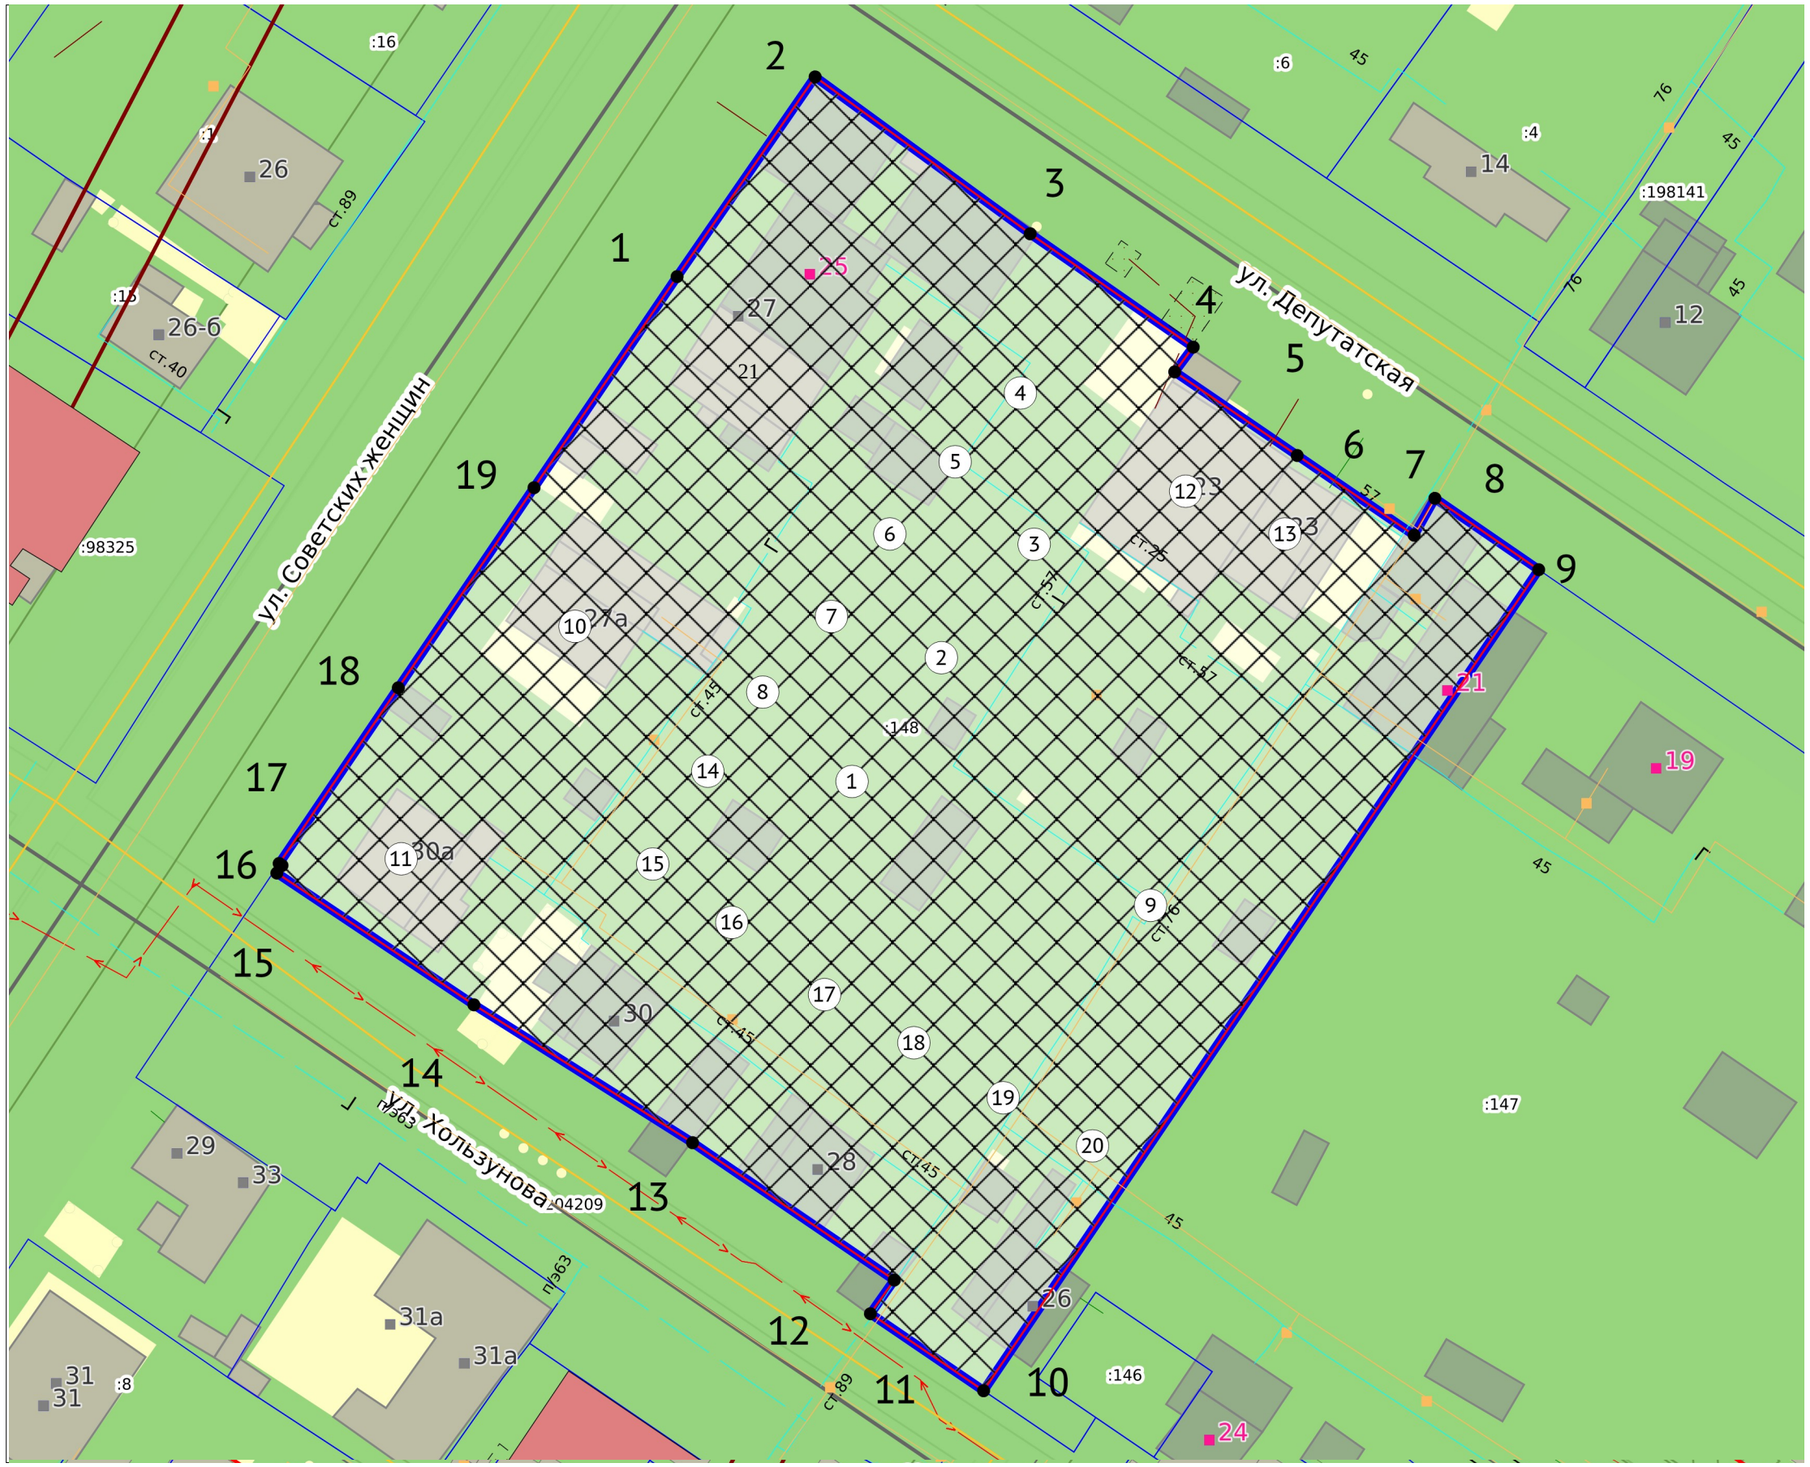

ЭКСПЛИКАЦИЯ ОБЪЕКТОВ

№ п/п	Наименование объекта
1	Место допустимого размещения объектов капитального строительства в соответствии с регламентами территориальной зоны Ж-5
2	Приаэродромная территория: Сектор 9 3 подзона ПАТ аэродрома Екатеринбург (Арамиль)
3	Приаэродромная территория: 1 Сектор, III Подзона Екатеринбург (Кольцово) (Набс = 383,50 м)
4	Приаэродромная территория: 60 Сектор, IV Подзона Екатеринбург (Кольцово) (Набс от 365,00 м до 367,40 м)
5	Приаэродромная территория: V Подзона Екатеринбург (Кольцово)
6	Приаэродромная территория: VI Подзона Екатеринбург (Кольцово)
7	Приаэродромная территория: III Подзона Екатеринбург (Кольцово)
8	Приаэродромная территория: IV Подзона Екатеринбург (Кольцово)
9	Объект капитального строительства №66:41:0000000:86963
10	Объект капитального строительства
11	Объект капитального строительства
12	Объект капитального строительства
13	Объект капитального строительства
14	Охранная зона транспорта №66:00-6.1909
15	Охранная зона транспорта №66:00-6.2651
16	Охранная зона транспорта №66:00-6.1907
17	Охранная зона транспорта №66:00-6.1908
18	Охранная зона транспорта №66:00-6.1915
19	Охранная зона транспорта №66:00-6.1910
20	Охранная зона транспорта №66:00-6.2648
21	Объект капитального строительства

УСЛОВНЫЕ ОБОЗНАЧЕНИЯ

- Место допустимого размещения
- Земельный участок ГПЗУ
- Земельные участки
- Здания, строения
- ЗОУИТ

Чертеж градостроительного плана земельного участка разработан на топографической основе, выполненной 2024

Чертеж градостроительного плана земельного участка разработан 13.08.2024
Отделом развития территории Департамента архитектуры, градостроительства и регулирования земельных отношений Администрации города Екатеринбурга

Кадастровый номер:	66:41:0403044:148		**№ РФ-66-3-02-0-00-2024-2185-0**
Площадь участка:	5498 м²		
Масштаб:	1:1000		Свердловская область, г Екатеринбург, ул Депутатская
Территориальная зона:	Ж-5, подзона 45.4		

Должность	*ФИО*	*Подпись*	*Дата*
Ведущий специалист	Волкова К.П.		13.08.2024
Зав.сектором подготовки град.планов	Лошманова Е.Г.		13.08.2024

1.ЧЕРТЕЖ ГРАДОСТРОИТЕЛЬНОГО ПЛАНАЗЕМЕЛЬНОГО УЧАСТКА

Раздел	*Лист*	*Листов*
1	2	2

Департамент архитектуры, градостроительства и регулирования земельных отношений Администрации города Екатеринбурга

2. Информация о градостроительном регламенте либо требованиях к назначению, параметрам и размещению объекта капитального строительства на земельном участке, на который действие градостроительного регламента не распространяется или для которого градостроительный регламент не устанавливается

Земельный участок расположен в Подзоне № 45.4 в пределах территориальной зоны – Ж-5 Зона многоэтажной жилой застройки. Установлен градостроительный регламент.

Действие градостроительного регламента, установленного в составе Правила землепользования и застройки городского округа - муниципального образования «город Екатеринбург», утверждены Решением Екатеринбургской городской Думы от 19 июня 2018года от №22/83, на земельные участки (территории) общего пользования не распространяется.

2.1. Реквизиты акта органа государственной власти субъекта Российской Федерации, органа местного самоуправления, содержащего градостроительный регламент либо реквизиты акта федерального органа государственной власти, органа государственной власти субъекта Российской Федерации, органа местного самоуправления, иной организации, определяющего, в соответствии с федеральными законами, порядок использования земельного участка, на который действие градостроительного регламента не распространяется или для которого градостроительный регламент не устанавливается

Постановление Администрации города Екатеринбурга от 10.06.2022 № 1597 "Об утверждении Правил землепользования и застройки городского округа - муниципального образования "город Екатеринбург"

2.2. Информация о видах разрешенного использования земельного участка:
Подзона № 45.4:

Основные виды разрешенного использования:
1. Магазины
2. Объекты торговли (торговые центры, торгово-развлекательные центры (комплексы)
3. Многоэтажная жилая застройка (высотная застройка)
4. Хранение автотранспорта
5. Земельные участки (территории) общего пользования
6. Коммунальное обслуживание
7. Внеуличный транспорт
8. Среднеэтажная жилая застройка
9. Дошкольное, начальное и среднее общее образование
10. Обеспечение внутреннего правопорядка
11. Здравоохранение
12. Спорт

Условно разрешенные виды использования земельного участка:
1. Историко-культурная деятельность
2. Производственная деятельность
3. Связь
4. Общежития
5. Социальное обслуживание
6. Бытовое обслуживание
7. Культурное развитие
8. Религиозное использование
9. Амбулаторное ветеринарное обслуживание
10. Деловое управление
11. Банковская и страховая деятельность
12. Общественное питание
13. Гостиничное обслуживание
14. Автомобильные мойки
15. Заправка транспортных средств

Вспомогательные виды разрешенного использования земельного участка:
1. Не подлежат установлению

2.3. Предельные (минимальные и (или) максимальные) размеры земельного участка и предельные параметры разрешенного строительства, реконструкции объекта капитального строительства, установленные градостроительным регламентом для территориальной зоны, в которой расположен земельный участок:

Предельные (минимальные и (или) максимальные) размеры земельных участков, в том числе их площадь			Минимальные отступы от границ земельного участка в целях определения мест допустимого размещения зданий, строений, сооружений, за пределами которых запрещено строительство зданий, строений, сооружений	Предельное количество этажей и (или) предельная высота зданий, строений, сооружений	Максимальный процент застройки в границах земельного участка, определяемый как отношение суммарной площади земельного участка, которая может быть застроена, ко всей площади земельного участка, %	Требования к архитектурным решениям объектов капитального строительства, расположенным в границах территории исторического поселения федерального или регионального значения	Иные показатели
1	**2**	**3**	**4**	**5**	**6**	**7**	**8**
Длина, м	Ширина, м	Площадь, м^2 или га					
Ж-5 Зона многоэтажной жилой застройки							
-	**-**	**-***	**-***	**-***	**-***		**-***

*- Земельный участок находится в пределах подзоны № 45.4.
В границах подзон № 45.1 – 45.10 предельные параметры разрешенного строительства, реконструкции объектов капитального строительства не подлежат установлению, за исключением общей площади жилых помещений, количества машино-мест, количества мест в дошкольных образовательных учреждениях.
В границах подзоны № 45.4 общая площадь жилых помещений – не более 20 810 кв. м, количество машино-мест – не менее 130.

* - Предельные (минимальные и (или) максимальные) размеры земельных участков и предельные параметры разрешенного строительства, реконструкции объектов многоэтажной жилой застройки:
минимальная площадь земельного участка - 3000 кв. м;
минимальные отступы от границ земельных участков в целях определения мест допустимого размещения зданий, строений, сооружений, за пределами которых запрещено строительство зданий, строений, сооружений не подлежат установлению;
предельное количество этажей или предельная высота зданий, строений, сооружений не подлежат установлению;
максимальный процент застройки в границах земельного участка, определяемый как отношение суммарной площади земельного участка, которая может быть застроена, ко всей площади земельного участка для многоэтажной жилой застройки – не подлежат установлению
Иные предельные параметры разрешенного строительства, реконструкции объектов капитального строительства многоэтажной жилой застройки:
коэффициент строительного использования земельного участка – не подлежат установлению
процент застройки подземного пространства – не подлежат установлению
- Предельные (минимальные и (или) максимальные) размеры земельных участков и предельные параметры разрешенного строительства, реконструкции объектов среднеэтажной жилой застройки:
минимальная площадь земельного участка – 1500 кв.м;
минимальные отступы от границ земельных участков в целях определения мест допустимого размещения зданий, строений, сооружений, за пределами которых запрещено строительство зданий, строений, сооружений не подлежат установлению;
предельное количество этажей или предельная высота зданий, строений, сооружений не подлежат установлению;
максимальный процент застройки в границах земельного участка, определяемый как отношение суммарной площади земельного участка, которая может быть застроена, ко всей площади земельного участка – не подлежат установлению
Иные предельные параметры разрешенного строительства, реконструкции объектов капитального строительства среднеэтажной жилой застройки:
коэффициент строительного использования земельного участка – не подлежат установлению
процент застройки подземного пространства – не подлежат установлению
- Предельные (минимальные и (или) максимальные) размеры иных земельных участков и предельные параметры разрешенного строительства, реконструкции для иных объектов капитального строительства:
предельные (минимальные и (или) максимальные) размеры земельных участков, в том числе их площадь не подлежат установлению;
минимальные отступы от границ земельных участков в целях определения мест допустимого размещения зданий, строений, сооружений, за пределами которых запрещено строительство зданий, строений, сооружений не подлежат установлению;
предельное количество этажей или предельная высота зданий, строений, сооружений (за исключением объектов бытового обслуживания, амбулаторно-ветеринарного обслуживания, делового управления, банковской и страховой деятельности, общественного питания и гостиничного обслуживания) не подлежат установлению;
предельное количество этажей для объектов бытового обслуживания – не подлежат установлению;
предельное количество этажей для объектов амбулаторно-ветеринарного обслуживания – не подлежат установлению;
предельное количество этажей для делового управления – не подлежат установлению;
предельное количество этажей для объектов банковской и страховой деятельности – не подлежат установлению
предельное количество этажей для объектов общественного питания – не подлежат установлению
предельное количество этажей для объектов гостиничного обслуживания – не подлежат установлению;
максимальный процент застройки в границах земельного участка, определяемый как отношение суммарной площади земельного участка, которая может быть застроена, ко всей площади земельного участка не подлежат установлению;
Иные предельные параметры разрешенного строительства, реконструкции иных объектов капитального строительства:
коэффициент строительного использования земельного участка – не подлежат установлению
процент застройки подземного пространства – не подлежат установлению
максимальная общая площадь объектов торговли (торговые центры, торгово-развлекательные центры (комплексы) - не подлежат установлению;
максимальная общая площадь объектов бытового обслуживания – не подлежат установлению
максимальная общая площадь объектов амбулаторно-ветеринарного обслуживания – не подлежат установлению
максимальная общая площадь объектов общественного питания – не подлежат установлению
максимальная общая площадь объектов гостиничного обслуживания – не подлежат установлению;

2.4. Требования к назначению, параметрам и размещению объекта капитального строительства на земельном участке, на который действие градостроительного регламента не распространяется или для которого градостроительный регламент не устанавливается (за исключением случая, предусмотренного пунктом 7.1 части 3 статьи 57.3 Градостроительного кодекса Российской Федерации):

Причины отнесения земельного участка к виду земельного участка, на который действие градостроительного регламента не распространяется или для которого градостроительный регламент не устанавливается	Реквизиты акта, регулирующего использование земельного участка	Требования к использованию земельного участка	Требования к параметрам объекта капитального строительства			Требования к размещению объектов капитального строительства	
			Предельное количество этажей и (или) предельная высота зданий, строений, сооружений	Максимальный процент застройки в границах земельного участка, определяемый как отношение суммарной площади земельного участка, которая может быть застроена, ко всей площади земельного участка	Иные требования к параметрам объекта капитального строительства	Минимальные отступы от границ земельного участка в целях определения мест допустимого размещения зданий, строений, сооружений, за пределами которых запрещено строительство зданий, строений, сооружений	Иные требования к размещению объектов капитального строительства
1	2	3	4	5	6	7	8
-	-	-	-	-	-	-	-

2.5.Предельные параметры разрешенного строительства, реконструкции объекта капитального строительства, установленные положением об особо охраняемых природных территориях, в случае выдачи градостроительного плана земельного участка в отношении земельного участка, расположенного в границах особо охраняемой природной территории:

Причины отнесения земельного участка к виду земельного участка для которого градостроительный регламент не устанавливается	Реквизиты Положения об особо охраняемой природной территории	Реквизиты утвержденной документации по планировке территории	Зонирование особо охраняемой природной территории (да/нет)								
			Функциональная зона	Виды разрешенного использования земельного участка		Требования к параметрам объекта капитального строительства			Требования к размещению объектов капитального строительства	
				Основные виды разрешенногоиспользования	Вспомогательные виды разрешенногоиспользования	Предельноеколичество этажей и (или) предельная высота зданий, строений, сооружений	Максимальный процент застройки в границах земельного участка, определяемый как отношение суммарной площади земельного участка, которая может быть застроена, ко всей площади земельного участка	Иные требования к параметрам объекта капитального строительства	Минимальные отступы от границ земельного участка в целях определения мест допустимогоразмещения зданий, строений, сооружений, за пределами которых запрещено строительство зданий, строений, сооружений	Иные требования к размещению объектов капитального строительства
1	2	3	4	5	6	7	8	9	10	11
-	-	-	-	-	-	-	-	-	-	-

3. Информация о расположенных в границах земельного участка объектах капитального строительства и объектах культурного наследия:

3.1. Объекты капитального строительства:

№ 9 (согласно чертежу(ам) градостроительного плана), Объект капитального строительства (назначение объекта капитального строительства, этажность, высотность, общая площадь, площадь застройки)

инвентаризационный или кадастровый номер 66:41:0000000:86963

№ 10 (согласно чертежу(ам) градостроительного плана), Объект капитального строительства (назначение объекта капитального строительства, этажность, высотность, общая площадь, площадь застройки)

инвентаризационный или кадастровый номер -

№ 11 (согласно чертежу(ам) градостроительного плана), Объект капитального строительства (назначение объекта капитального строительства, этажность, высотность, общая площадь, площадь застройки)

инвентаризационный или кадастровый номер -

№ 12 (согласно чертежу(ам) градостроительного плана), Объект капитального строительства (назначение объекта капитального строительства, этажность, высотность, общая площадь, площадь застройки)

инвентаризационный или кадастровый номер -

№

13

,

Объект капитального строительства

,

(согласно чертежу(ам) градостроительного плана)

(назначение объекта капитального строительства, этажность, высотность, общая площадь, площадь застройки)

инвентаризационный или кадастровый номер

-

№

21

,

Объект капитального строительства

,

(согласно чертежу(ам) градостроительного плана)

(назначение объекта капитального строительства, этажность, высотность, общая площадь, площадь застройки)

инвентаризационный или кадастровый номер -

3.2. Объекты, включенные в единый государственный реестр объектов культурного наследия (памятников истории и культуры) народов Российской Федерации

№ - , Информация отсутствует ,
(согласно чертежу(ам) градостроительного плана) (назначение объекта культурного наследия, общая площадь, площадь застройки)

-
(наименование органа государственной власти, принявшего решение о включении выявленного объекта культурного наследия в реестр, реквизиты этого решения)
регистрационный номер в реестре - от -
(дата)

4. Информация о расчетных показателях минимально допустимого уровня обеспеченности территории объектами коммунальной, транспортной, социальной инфраструктур и расчетных показателях максимально допустимого уровня территориальной доступности указанных объектов для населения в случае, если земельный участок расположен в границах территории, в отношении которой предусматривается осуществление деятельности по комплексному и устойчивому развитию территории:

:

Информация о расчетных показателях минимально допустимого уровня обеспеченности территории		
Объекты коммунальной инфраструктуры		
Наименование вида объекта	Единица измерения	Расчетный показатель
Объекты транспортной инфраструктуры		
Наименование вида объекта	Единица измерения	Расчетный показатель
Объекты социальной инфраструктуры		
Наименование вида объекта	Единица измерения	Расчетный показатель

5. Информация об ограничениях использования земельного участка, в том числе если земельный участок полностью или частично расположен в границах зон с особыми условиями использования территорий

5.1. Ограничения использования земельного участка:

В соответствии с данными Единого государственного реестра недвижимости земельный участок полностью или частично расположен в границах зоны(-он) с особыми условиями использования территории:

- Охранная зона транспорта 66:00-6.1908.

Ограничения: Запрещается размещать объекты, создающие помехи в работе наземных объектов средств и систем обслуживания воздушного движения, навигации, посадки и связи, предназначенных для организации воздушного движения и расположенных вне первой подзоны.;

- Охранная зона транспорта 66:00-6.1907.

Ограничения: Запрещается размещать объекты, высота которых превышает ограничения, установленные уполномоченным Правительством Российской Федерации федеральным органом исполнительной власти при установлении соответствующей приаэродромной территории.;

- Охранная зона транспорта 66:00-6.2648.

Ограничения: Ограничения в третьей подзоне ПАТ аэродрома Екатеринбург (Арамиль) устанавливаются в соответствии с подпунктом 3 пункта 3 статьи 47 Воздушного кодекса Российской Федерации (Собрание законодательства Российской Федерации, 1997, № 12, ст. 1383; 2021, № 24, ст. 4209). В третьей подзоне устанавливаются ограничения на размещение объектов, высота которых превышает установленные ограничения. Высота препятствий ограничивается в пределах полос воздушных подходов, а также на участках, прилегающих к боковым границам летного поля и полос воздушных подходов. Ограничения представляют собой условные плоскости, параметры которых приведены ниже. 29.1. В пределах полос воздушных подходов, состоящих из трех участков:1-й участок длиной 400 метров, имеющий наклон 0,5%; 2-й участок длиной 950 метров, имеющий наклон 1,9%; 3-й участок длиной 9000 метров, имеющий наклон 2%. 29.2. За пределами полос воздушных подходов: поверхность вдоль летного поля, имеющая наклон 10%; горизонтальная поверхность на высоте 50 метров; поверхность от горизонтальной поверхности (50 м) до горизонтальной поверхности (200 м), имеющая наклон 4%. Горизонтальная поверхность на

высоте 200 метров, имеющая размеры 40 км в длину (вдоль оси взлетно-посадочной полосы (далее – ВПП) и 30 км в ширину (вдоль перпендикуляра к оси ВПП). На территории третьей подзоны выделяются 9 секторов. Во всех секторах ограничивается абсолютная высота объектов. Ограничения действуют для вновь создаваемых объектов, для реконструируемых объектов в части увеличения высоты. Запрещается размещать объекты, высота которых превышает ограничения, установленные в секторах третьей подзоны;

Реквизиты акта, установившего соответствующие ограничения: Приказ «Об установлении приаэродромной территории аэродрома Екатеринбург (Арамиль)» № 277 от 2022-08-15 Орган, выдавший документ: Федеральная служба войск национальной гвардии Российской Федерации; Приказ «О внесении изменений в приаэродромную территорию аэродрома Екатеринбург (Арамиль), утвержденную приказом Федеральной службы войск национальной гвардии Российской Федерации от 15 августа 2022 г. № 277» № 185 от 2023-06-02 Орган, выдавший документ: Федеральная служба войск национальной гвардии Российской Федерации.

- Охранная зона транспорта 66:00-6.2651.

Ограничения: Реквизиты акта, установившего соответствующие ограничения: Приказ «Об установлении приаэродромной территории аэродрома Екатеринбург (Арамиль)» № 277 от 2022-08-15 Орган, выдавший документ: Федеральная служба войск национальной гвардии Российской Федерации; Приказ «О внесении изменений в приаэродромную территорию аэродрома Екатеринбург (Арамиль), утвержденную приказом Федеральной службы войск национальной гвардии Российской Федерации от 15 августа 2022 г. № 277» № 185 от 2023-06-02 Орган, выдавший документ: Федеральная служба войск национальной гвардии Российской Федерации.

- Охранная зона транспорта 66:00-6.1910.

Ограничения: В границах шестой подзоны запрещается размещение объектов, способствующих привлечению и массовому скоплению птиц: зернохранилищ и предприятий по переработке зерна (элеваторы, мельницы), предприятий по производству кормов открытого типа, звероводческих ферм, скотобоен, свинарников, коровников, птицеферм, свалок и любых объектов обращения с отходами, мест разведения птиц, рыбных хозяйств, скотомогильников и других объектов и/или осуществление видов деятельности, способствующих массовому скоплению птиц, в соответствии с законодательством РФ. Допускается осуществление деятельности и сохранение существующих в границах шестой подзоны объектов, их эксплуатация (в том числе капитальный ремонт, модернизация, техническое перевооружение, реконструкция) при условии проведения мероприятий по предупреждению скопления птиц в соответствии с требованиями законодательства РФ, с учетом эколого-орнитологических заключений в соответствии с законодательством РФ.;

- Приаэродромная территория аэродрома Екатеринбург (Кольцово) 66:00-6.1915.

Ограничения: Ограничения указаны в Приказе Федерального агентства воздушного транспорта "Об установлении Приаэродромной территория аэродрома Екатеринбург (Кольцово)" от 03.12.2021 № 928-П.;

- Охранная зона транспорта 66:00-6.1909.

Ограничения: Запрещено размещение опасных производственных объектов 1 – 2 классов опасности согласно федеральному закону от 21.07.1997 №116-ФЗ «О промышленной безопасности опасных производственных объектов», и газопроводов проектным рабочим давлением свыше 0,6 МПа, функционирование которых может повлиять на безопасность полетов воздушных судов. Допускается размещение (строительство, реконструкция и эксплуатация) указанных объектов и газопроводов проектным рабочим давлением свыше 0,6 МПа на основании декларации промышленной безопасности с учетом оценки и их влияния на безопасность полетов воздушных судов, и (при необходимости) специальных технических условий, содержащих дополнительные технические требования, обеспечивающие безопасную эксплуатацию и функционирование объектов и сооружений, в том числе безопасность полетов воздушных судов.;

В соответствии с данными информационной системы обеспечения градостроительной деятельности земельный участок с кадастровым номером 66:41:0403044:148 расположен в границах зон с особыми условиями использования территории, не установленной в соответствии с федеральным законодательством (не зарегистрированы в Едином государственном реестре недвижимости):

– Приаэродромная территория: Сектор 9 3 подзона ПАТ аэродрома Екатеринбург (Арамиль), Приказ Об установлении приаэродромной территории аэродрома Екатеринбург (Арамиль) №277 от 15.08.2022.

Ограничения: 423,58 - Ограничение абсолютной высоты, м;

– Приаэродромная территория: 1 Сектор, III Подзона Екатеринбург (Кольцово) (Набс = 383,50 м), Приказ Росавиации № 367-П от 02.06.2023 Об установлении приаэродромной территории аэродрома гражданской авиации Екатеринбург (Кольцово) №367-П от 02.06.2023.

Ограничения: Строительство и реконструкция зданий, сооружений в границах третьей подзоны разрешается только после определения максимально допустимой высоты здания, сооружения в зависимости от местоположения путем проведения соответствующих расчетов в соответствии с требованиями ФАП-262 с учетом следующих абсолютных высот ограничения объектов в Балтийской системе высот 1977 года: 383,50 м;

– Приаэродромная территория: 60 Сектор, IV Подзона Екатеринбург (Кольцово) (Набс от 365,00 м до 367,40 м), Приказ Росавиации № 367-П от 02.06.2023 Об установлении приаэродромной территории аэродрома гражданской авиации Екатеринбург (Кольцово) №367-П от 02.06.2023.

Ограничения: 1. Запрещается размещать объекты, создающие помехи в работе наземных объектов средств и систем обслуживания воздушного движения, навигации, посадки и связи, предназначенных для организации воздушного движения и расположенных вне первой подзоны. 2. Запрещается без согласования с оператором аэдрома размещение объектов, превышающих высотные ограничения в границах установленных секторов: от 365,00 м до 367,40 м;

– Приаэродромная территория: V Подзона Екатеринбург (Кольцово) , Приказ Росавиации № 367-П от 02.06.2023 Об установлении приаэродромной территории аэродрома гражданской авиации Екатеринбург (Кольцово) №367-П от 02.06.2023.

Ограничения: 1. В границах пятой подзоны запрещается размещать опасные производственные объекты, функционирование которых может повлиять на безопасность полетов воздушных судов. 2. В границах пятой подзоны допускается эксплуатация, строительство, реконструкция, капитальный ремонт, техническое перевооружение, консервация (далее размещение) опасных производственных объектов при их соответствии установленным в пункте 3 ограничениям. 3. Максимальные радиусы зон поражения при происшествиях техногенного характера на опасных производственных объектах, находящихся в пятой подзоне приаэродромной территории, в которых размещение таких объектов возможно, не должны достигать: по вертикали - высоты пролета воздушных судов (высота поверхности ограничения препятствий в третьей подзоне приаэродромной территории); по горизонтали - внешних границ первой и второй подзон приаэродромной территории аэродрома. 4. При невозможности соблюдения ограничений, предусмотренных пунктом 3, размещение опасных производственных объектов должно выполняться на основании специальных технических условий, разработанных для конкретного объекта капитального строительства в соответствии с положениями приказа Минстроя России от 30 ноября 2020 г. № 734/пр "Об утверждении порядка разработки и согласования специальных технических условий для разработчики проектной документации на объект капитального строительства".;

– Приаэродромная территория: VI Подзона Екатеринбург (Кольцово) , Приказ Росавиации № 367-П от 02.06.2023 Об установлении приаэродромной территории аэродрома гражданской авиации Екатеринбург (Кольцово) №367-П от 02.06.2023.

Ограничения: В границах шестой подзоны приаэродромной территории запрещается размещать объекты, способствующие привлечению и массовому скоплению птиц.;

– Приаэродромная территория: III Подзона Екатеринбург (Кольцово) , Приказ Росавиации № 367-П от 02.06.2023 Об установлении приаэродромной территории аэродрома гражданской авиации Екатеринбург (Кольцово) №367-П от 02.06.2023.

Ограничения: В границах третьей подзоны запрещается размещать объекты, высота которых прпевышает ограничения;

– Приаэродромная территория: IV Подзона Екатеринбург (Кольцово) , Приказ Росавиации № 367-П от 02.06.2023 Об установлении приаэродромной территории аэродрома гражданской авиации Екатеринбург (Кольцово) №367-П от 02.06.2023.

Ограничения: Запрещается размещать объекты, создающие помехи в работе наземных объектов средств и систем обслуживания воздушного движения, навигации, посадки и связи, предназначенных для организации воздушного движения и расположенных вне первой подзоны. Запрещается без согласования с оператором аэродрома размещение объектов, превышающих высотные ограничения;

В целях актуализации информации о наличии или отсутствии сетей инженерно- технического обеспечения на земельном участке с кадастровым номером: 66:41:0403044:148 правообладателю земельного участка в соответствии с пунктом 1 статьи 47 Градостроительного Кодекса Российской Федерации в редакции от 29.07.2017 № 280-ФЗ рекомендуется провести инженерные изыскания для подготовки проектной документации.

Размещение объектов капитального строительства на земельном участке с кадастровым номером: 66:41:0403044:148 возможно при условии переустройства (выноса) существующих сетей инженерно-технического обеспечения или согласования размещения объектов капитального строительства в охранных зонах (зонах ограничения застройки) в соответствии с техническими условиями балансодержателей сетей, в том числе при соблюдении требований к параметрам зданий и сооружений, установленных Постановлением Правительства Российской Федерации от 24.02.2009 № 160.

5.2. Иные сведения:

1. Земельный участок полностью расположен в границах полос воздушных подходов аэродрома гражданской авиации: Екатеринбург (Кольцово), утвержденный приказом Федерального агентства воздушного транспорта от 07.02.2020 №135-П.

2. Необходимо соблюдать специальные требования, установленные нормативно-техническими документами в зоне охраны сетей инженерно-технического обеспечения.

3. В соответствии с п. 4 ст. 36 Федерального закона от 25 июня 2002 года № 73-ФЗ «Об объектах культурного наследия (памятниках истории и культуры) народов Российской Федерации» в случае обнаружения в ходе проведения изыскательских, проектных, земляных, строительных, мелиоративных, хозяйственных и иных работ объекта, обладающего признаками объекта культурного наследия, в том числе объекта археологического наследия, заказчик указанных работ, технический заказчик (застройщик) объекта капитального строительства, лицо, проводящее указанные работы, обязаны незамедлительно приостановить указанные работы и в течение трех дней со дня обнаружения такого объекта направить в орган исполнительной власти субъекта Российской Федерации, уполномоченный в области охраны объектов культурного наследия, письменное заявление об обнаруженном объекте.

4. Размещение внешних инженерных сетей подлежит согласованию с землепользователями. Информация о землепользователях содержится в информационной справке. При необходимости трассировку внешних инженерных сетей решить ситуационным планом размещения сети инженерно-технического обеспечения на кадастровом плане территории.

6. Информация о границах зон с особыми условиями использования территорий, если земельный участок полностью или частично расположен в границах таких зон: см. Приложение №1

7. Информация о границах публичных сервитутов: см. Приложение №1

8. Номер и (или) наименование элемента планировочной структуры, в границах которого расположен земельный участок

9. Информация о технических условиях подключения (технологического присоединения) объектов капитального строительства к сетям инженерно-технического обеспечения, определенных с учетом программ комплексного развития систем коммунальной инфраструктуры поселения, городского округа

Номер объекта	Назначение объекта	Сети инженерно-технического обеспечения объекта	Наименование органа (организации), выдавшего технические условия	Дата выдачи технических условий
1	2	3	4	5
1	Объект в соответствии с регламентами территориальной зоны Ж-5	Водоснабжение и водоотведение хозяйственно-бытовых стоков	ЕМУП «Водоканал»	технические условия отсутствуют*
		Электроснабжение	АО «Екатеринбургская электросетевая компания»	технические условия отсутствуют*
		Теплоснабжение	АО «Екатеринбургская теплосетевая компания»	технические условия отсутствуют*
		Отвод дождевых и дренажных стоков	МБУ «ВОИС»	технические условия отсутствуют*

* Правообладатель в целях определения необходимой ему подключаемой нагрузки обращается в организацию, осуществляющую эксплуатацию сетей инженерно-технического обеспечения, к которым планируется подключение строящегося, реконструируемого (построенного) объекта капитального строительства, для получения технических условий с учетом актуализированной схемы теплоснабжения муниципального образования «город Екатеринбург» до 2030 года, утвержденной Приказом Министерства энергетики Российской Федерации от 30.12.2021 № 1542, программы комплексного развития систем коммунальной инфраструктуры муниципального образования «город Екатеринбург» на 2016 – 2025 годы, утвержденной Решением Екатеринбургской городской Думы от 28.06.2016 № 21/52, схем водоснабжения и водоотведения муниципального образования «город Екатеринбург» до 2025 года, утвержденных Постановлением Администрации города Екатеринбурга от 30.12.2014 № 4077, инвестиционных программ организаций коммунального комплекса. В соответствии с утвержденными схемами инженерно-технического обеспечения на территории муниципального образования «город Екатеринбург» могут быть определены иные организации коммунального комплекса с зонами действия (покрытия) источников, выдающие технические условия. Срок действия технических условий устанавливается организациями, осуществляющими эксплуатацию сетей инженерно-технического обеспечения, не менее чем на три года или при комплексном освоении земельных участков в целях жилищного строительства не менее чем на пять лет.

10. Реквизиты нормативных правовых актов субъекта Российской Федерации, муниципальных правовых актов, устанавливающих требования к благоустройству территории

11. Информация о красных линиях: см. Приложение №1

Описание границ земельного участка (образуемого земельного участка)
(раздел 1 лист 2 градостроительного плана земельного участка):

Обозначение (номер) характерной точки	Перечень координат характерных точек в системе координат, используемой для ведения Единого государственного реестра недвижимости	
	X	Y
1	387509.92	1532936.30
2	387526.19	1532947.55
3	387513.41	1532965.08
4	387504.18	1532978.36
5	387502.16	1532976.86
6	387495.35	1532986.84
7	387488.86	1532996.37
8	387491.86	1532998.06
9	387486.05	1533006.52
10	387419.18	1532961.28
11	387425.45	1532952.06
12	387428.19	1532954.00
13	387439.38	1532937.56
14	387450.61	1532919.74
15	387461.34	1532903.68
16	387461.96	1532904.10
17	387462.12	1532903.87
18	387476.43	1532913.58
19	387492.73	1532924.64
1	387509.92	1532936.30

Информация о границах зоны планируемого размещения объекта капитального строительства в соответствии с утвержденным проектом планировки территории (при наличии)
(раздел 1 лист 2 градостроительного плана земельного участка):
Проект планировки территории не утвержден

Обозначение (номер) характерной точки	Перечень координат характерных точек в системе координат, используемой для ведения Единого государственного реестра недвижимости	
	X	Y
-	-	-

Информация о границах зон с особыми условиями использования территорий, если земельный участок полностью или частично расположен в границах таких зон

(раздел 6 градостроительного плана земельного участка):

Наименование зоны с особыми условиями использования территории с указанием объекта, в отношении которого установлена такая зона	Перечень координат характерных точек в системе координат, используемой для ведения Единого государственного реестра недвижимости		
	Обозначение (номер) характерной точки	X	Y
1	2	3	4
Подзона 4 приаэродромной территории аэродрома Екатеринбург (Кольцово) (ЕГРН)	1	387509,92	1532936,30
	2	387526,19	1532947,55
	3	387513,41	1532965,08
	4	387504,18	1532978,36
	5	387502,16	1532976,86
	6	387495,35	1532986,84
	7	387488,86	1532996,37
	8	387491,86	1532998,06
	9	387486,05	1533006,52
	10	387419,18	1532961,28
	11	387425,45	1532952,06
	12	387428,19	1532954,00
	13	387439,38	1532937,56
	14	387450,61	1532919,74
	15	387461,34	1532903,68
	16	387461,96	1532904,10
	17	387462,12	1532903,87
	18	387476,43	1532913,58
	19	387492,73	1532924,64
Подзона 3 приаэродромной территории аэродрома Екатеринбург (Кольцово) (ЕГРН)	1	387509,92	1532936,30
	2	387526,19	1532947,55
	3	387513,41	1532965,08
	4	387504,18	1532978,36
	5	387502,16	1532976,86
	6	387495,35	1532986,84
	7	387488,86	1532996,37
	8	387491,86	1532998,06
	9	387486,05	1533006,52
	10	387419,18	1532961,28
	11	387425,45	1532952,06
	12	387428,19	1532954,00
	13	387439,38	1532937,56
	14	387450,61	1532919,74
	15	387461,34	1532903,68
	16	387461,96	1532904,10
	17	387462,12	1532903,87
	18	387476,43	1532913,58
	19	387492,73	1532924,64
Третья подзона приаэродромной территории Аэродрома Екатеринбург (Арамиль) (ЕГРН)	1	387509,92	1532936,30
	2	387526,19	1532947,55
	3	387513,41	1532965,08
	4	387504,18	1532978,36
	5	387502,16	1532976,86
	6	387495,35	1532986,84
	7	387488,86	1532996,37
	8	387491,86	1532998,06
	9	387486,05	1533006,52
	10	387419,18	1532961,28
	11	387425,45	1532952,06
	12	387428,19	1532954,00

	13 14 15 16 17 18 19	387439,38 387450,61 387461,34 387461,96 387462,12 387476,43 387492,73	1532937,56 1532919,74 1532903,68 1532904,10 1532903,87 1532913,58 1532924,64
приаэродромная территория Аэродрома Екатеринбург (Арамиль) (ЕГРН)	1 2 3 4 5 6 7 8 9 10 11 12 13 14 15 16 17 18 19	387509,92 387526,19 387513,41 387504,18 387502,16 387495,35 387488,86 387491,86 387486,05 387419,18 387425,45 387428,19 387439,38 387450,61 387461,34 387461,96 387462,12 387476,43 387492,73	1532936,30 1532947,55 1532965,08 1532978,36 1532976,86 1532986,84 1532996,37 1532998,06 1533006,52 1532961,28 1532952,06 1532954,00 1532937,56 1532919,74 1532903,68 1532904,10 1532903,87 1532913,58 1532924,64
Подзона 6 приаэродромной территории аэродрома Екатеринбург (Кольцово) (ЕГРН)	1 2 3 4 5 6 7 8 9 10 11 12 13 14 15 16 17 18 19	387509,92 387526,19 387513,41 387504,18 387502,16 387495,35 387488,86 387491,86 387486,05 387419,18 387425,45 387428,19 387439,38 387450,61 387461,34 387461,96 387462,12 387476,43 387492,73	1532936,30 1532947,55 1532965,08 1532978,36 1532976,86 1532986,84 1532996,37 1532998,06 1533006,52 1532961,28 1532952,06 1532954,00 1532937,56 1532919,74 1532903,68 1532904,10 1532903,87 1532913,58 1532924,64
Приаэродромная территория аэродрома Екатеринбург (Кольцово) (ЕГРН)	1 2 3 4 5 6 7 8 9 10 11 12	387509,92 387526,19 387513,41 387504,18 387502,16 387495,35 387488,86 387491,86 387486,05 387419,18 387425,45 387428,19	1532936,30 1532947,55 1532965,08 1532978,36 1532976,86 1532986,84 1532996,37 1532998,06 1533006,52 1532961,28 1532952,06 1532954,00

	13	387439,38	1532937,56
	14	387450,61	1532919,74
	15	387461,34	1532903,68
	16	387461,96	1532904,10
	17	387462,12	1532903,87
	18	387476,43	1532913,58
	19	387492,73	1532924,64
Подзона 5 приаэродромной территории аэродрома Екатеринбург (Кольцово) (ЕГРН)	1	387509,92	1532936,30
	2	387526,19	1532947,55
	3	387513,41	1532965,08
	4	387504,18	1532978,36
	5	387502,16	1532976,86
	6	387495,35	1532986,84
	7	387488,86	1532996,37
	8	387491,86	1532998,06
	9	387486,05	1533006,52
	10	387419,18	1532961,28
	11	387425,45	1532952,06
	12	387428,19	1532954,00
	13	387439,38	1532937,56
	14	387450,61	1532919,74
	15	387461,34	1532903,68
	16	387461,96	1532904,10
	17	387462,12	1532903,87
	18	387476,43	1532913,58
	19	387492,73	1532924,64
Сектор 9 3 подзона ПАТ аэродрома Екатеринбург (Арамиль) (Приказ Об установлении приаэродромной территории аэродрома Екатеринбург (Арамиль) №277 от 15.08.2022)	1	387509,92	1532936,30
	2	387526,19	1532947,55
	3	387513,41	1532965,08
	4	387504,18	1532978,36
	5	387502,16	1532976,86
	6	387495,35	1532986,84
	7	387488,86	1532996,37
	8	387491,86	1532998,06
	9	387486,05	1533006,52
	10	387419,18	1532961,28
	11	387425,45	1532952,06
	12	387428,19	1532954,00
	13	387439,38	1532937,56
	14	387450,61	1532919,74
	15	387461,34	1532903,68
	16	387461,96	1532904,10
	17	387462,12	1532903,87
	18	387476,43	1532913,58
	19	387492,73	1532924,64
1 Сектор, III Подзона Екатеринбург (Кольцово) (Набс = 383,50 м) (Приказ Росавиации № 367-П от 02.06.2023 Об установлении приаэродромной территории аэродрома гражданской авиации Екатеринбург (Кольцово) №367-П от 02.06.2023)	1	387509,92	1532936,30
	2	387526,19	1532947,55
	3	387513,41	1532965,08
	4	387504,18	1532978,36
	5	387502,16	1532976,86
	6	387495,35	1532986,84
	7	387488,86	1532996,37
	8	387491,86	1532998,06
	9	387486,05	1533006,52
	10	387419,18	1532961,28
	11	387425,45	1532952,06
	12	387428,19	1532954,00

	13	387439,38	1532937,56
	14	387450,61	1532919,74
	15	387461,34	1532903,68
	16	387461,96	1532904,10
	17	387462,12	1532903,87
	18	387476,43	1532913,58
	19	387492,73	1532924,64
60 Сектор, IV Подзона Екатеринбург (Кольцово) (Набс от 365,00 м до 367,40 м) (Приказ Росавиации № 367-П от 02.06.2023 Об установлении приаэродромной территории аэродрома гражданской авиации Екатеринбург (Кольцово) №367-П от 02.06.2023)	1	387509,92	1532936,30
	2	387526,19	1532947,55
	3	387513,41	1532965,08
	4	387504,18	1532978,36
	5	387502,16	1532976,86
	6	387495,35	1532986,84
	7	387488,86	1532996,37
	8	387491,86	1532998,06
	9	387486,05	1533006,52
	10	387419,18	1532961,28
	11	387425,45	1532952,06
	12	387428,19	1532954,00
	13	387439,38	1532937,56
	14	387450,61	1532919,74
	15	387461,34	1532903,68
	16	387461,96	1532904,10
	17	387462,12	1532903,87
	18	387476,43	1532913,58
	19	387492,73	1532924,64
V Подзона Екатеринбург (Кольцово) (Приказ Росавиации № 367-П от 02.06.2023 Об установлении приаэродромной территории аэродрома гражданской авиации Екатеринбург (Кольцово) №367-П от 02.06.2023)	1	387509,92	1532936,30
	2	387526,19	1532947,55
	3	387513,41	1532965,08
	4	387504,18	1532978,36
	5	387502,16	1532976,86
	6	387495,35	1532986,84
	7	387488,86	1532996,37
	8	387491,86	1532998,06
	9	387486,05	1533006,52
	10	387419,18	1532961,28
	11	387425,45	1532952,06
	12	387428,19	1532954,00
	13	387439,38	1532937,56
	14	387450,61	1532919,74
	15	387461,34	1532903,68
	16	387461,96	1532904,10
	17	387462,12	1532903,87
	18	387476,43	1532913,58
	19	387492,73	1532924,64
VI Подзона Екатеринбург (Кольцово) (Приказ Росавиации № 367-П от 02.06.2023 Об установлении приаэродромной территории аэродрома гражданской авиации Екатеринбург (Кольцово) №367-П от 02.06.2023)	1	387509,92	1532936,30
	2	387526,19	1532947,55
	3	387513,41	1532965,08
	4	387504,18	1532978,36
	5	387502,16	1532976,86
	6	387495,35	1532986,84
	7	387488,86	1532996,37
	8	387491,86	1532998,06
	9	387486,05	1533006,52
	10	387419,18	1532961,28
	11	387425,45	1532952,06
	12	387428,19	1532954,00

	13 14 15 16 17 18 19	387439,38 387450,61 387461,34 387461,96 387462,12 387476,43 387492,73	1532937,56 1532919,74 1532903,68 1532904,10 1532903,87 1532913,58 1532924,64
III Подзона Екатеринбург (Кольцово) (Приказ Росавиации № 367-П от 02.06.2023 Об установлении приаэродромной территории аэродрома гражданской авиации Екатеринбург (Кольцово) №367-П от 02.06.2023)	1 2 3 4 5 6 7 8 9 10 11 12 13 14 15 16 17 18 19	387509,92 387526,19 387513,41 387504,18 387502,16 387495,35 387488,86 387491,86 387486,05 387419,18 387425,45 387428,19 387439,38 387450,61 387461,34 387461,96 387462,12 387476,43 387492,73	1532936,30 1532947,55 1532965,08 1532978,36 1532976,86 1532986,84 1532996,37 1532998,06 1533006,52 1532961,28 1532952,06 1532954,00 1532937,56 1532919,74 1532903,68 1532904,10 1532903,87 1532913,58 1532924,64
IV Подзона Екатеринбург (Кольцово) (Приказ Росавиации № 367-П от 02.06.2023 Об установлении приаэродромной территории аэродрома гражданской авиации Екатеринбург (Кольцово) №367-П от 02.06.2023)	1 2 3 4 5 6 7 8 9 10 11 12 13 14 15 16 17 18 19	387509,92 387526,19 387513,41 387504,18 387502,16 387495,35 387488,86 387491,86 387486,05 387419,18 387425,45 387428,19 387439,38 387450,61 387461,34 387461,96 387462,12 387476,43 387492,73	1532936,30 1532947,55 1532965,08 1532978,36 1532976,86 1532986,84 1532996,37 1532998,06 1533006,52 1532961,28 1532952,06 1532954,00 1532937,56 1532919,74 1532903,68 1532904,10 1532903,87 1532913,58 1532924,64

Информация о границах публичных сервитутов
(раздел 7 градостроительного плана земельного участка) Информация отсутствует

Обозначение (номер) характерной точки	Перечень координат характерных точек в системе координат, используемой для ведения Единого государственного реестра недвижимости	
	X	Y
-	-	-

Информация о красных линиях
(раздел 11 градостроительного плана земельного участка)
Информация отсутствует

Обозначение (номер) характерной точки	Перечень координат характерных точек в системе координат, используемой для ведения Единого государственного реестра недвижимости	
	X	Y
-	-	-

Информация о требованиях к архитектурно-градостроительному облику объекта капитального строительства
(раздел 12 градостроительного плана земельного участка)
Требования к архитектурно-градостроительному облику объекта капитального строительства не установлены

№	Требования к архитектурно-градостроительному облику объекта капитального строительства	Показатель
1	2	3
-	-	-

ДОКУМЕНТ ПОДПИСАН
ЭЛЕКТРОННОЙ ПОДПИСЬЮ

Сертификат a4407f1890cd2f1730cd0e39ec8899a0
Владелец Габдрахманов Руслан Гайнельзянович
Действителен с 13.03.24 16:37:57 по 06.06.25 16:37:57